



Notes: ANY DISCREPANCY IN THIS DRAWING OR ANY OTHER DRAWINGS RELATED TO THIS DRAWING SHALL BE BROUGHT TO THE NOTICE OF THE ARCHITECT BEFORE COMMENCEMENT OF WORK


© THIS DRAWING IS THE PROPERTY OF VIDHRITA STUDIO ARCHITECTS AND IS NOT TO BE COPIED OR USED WITHOUT THEIR PERMISSION.

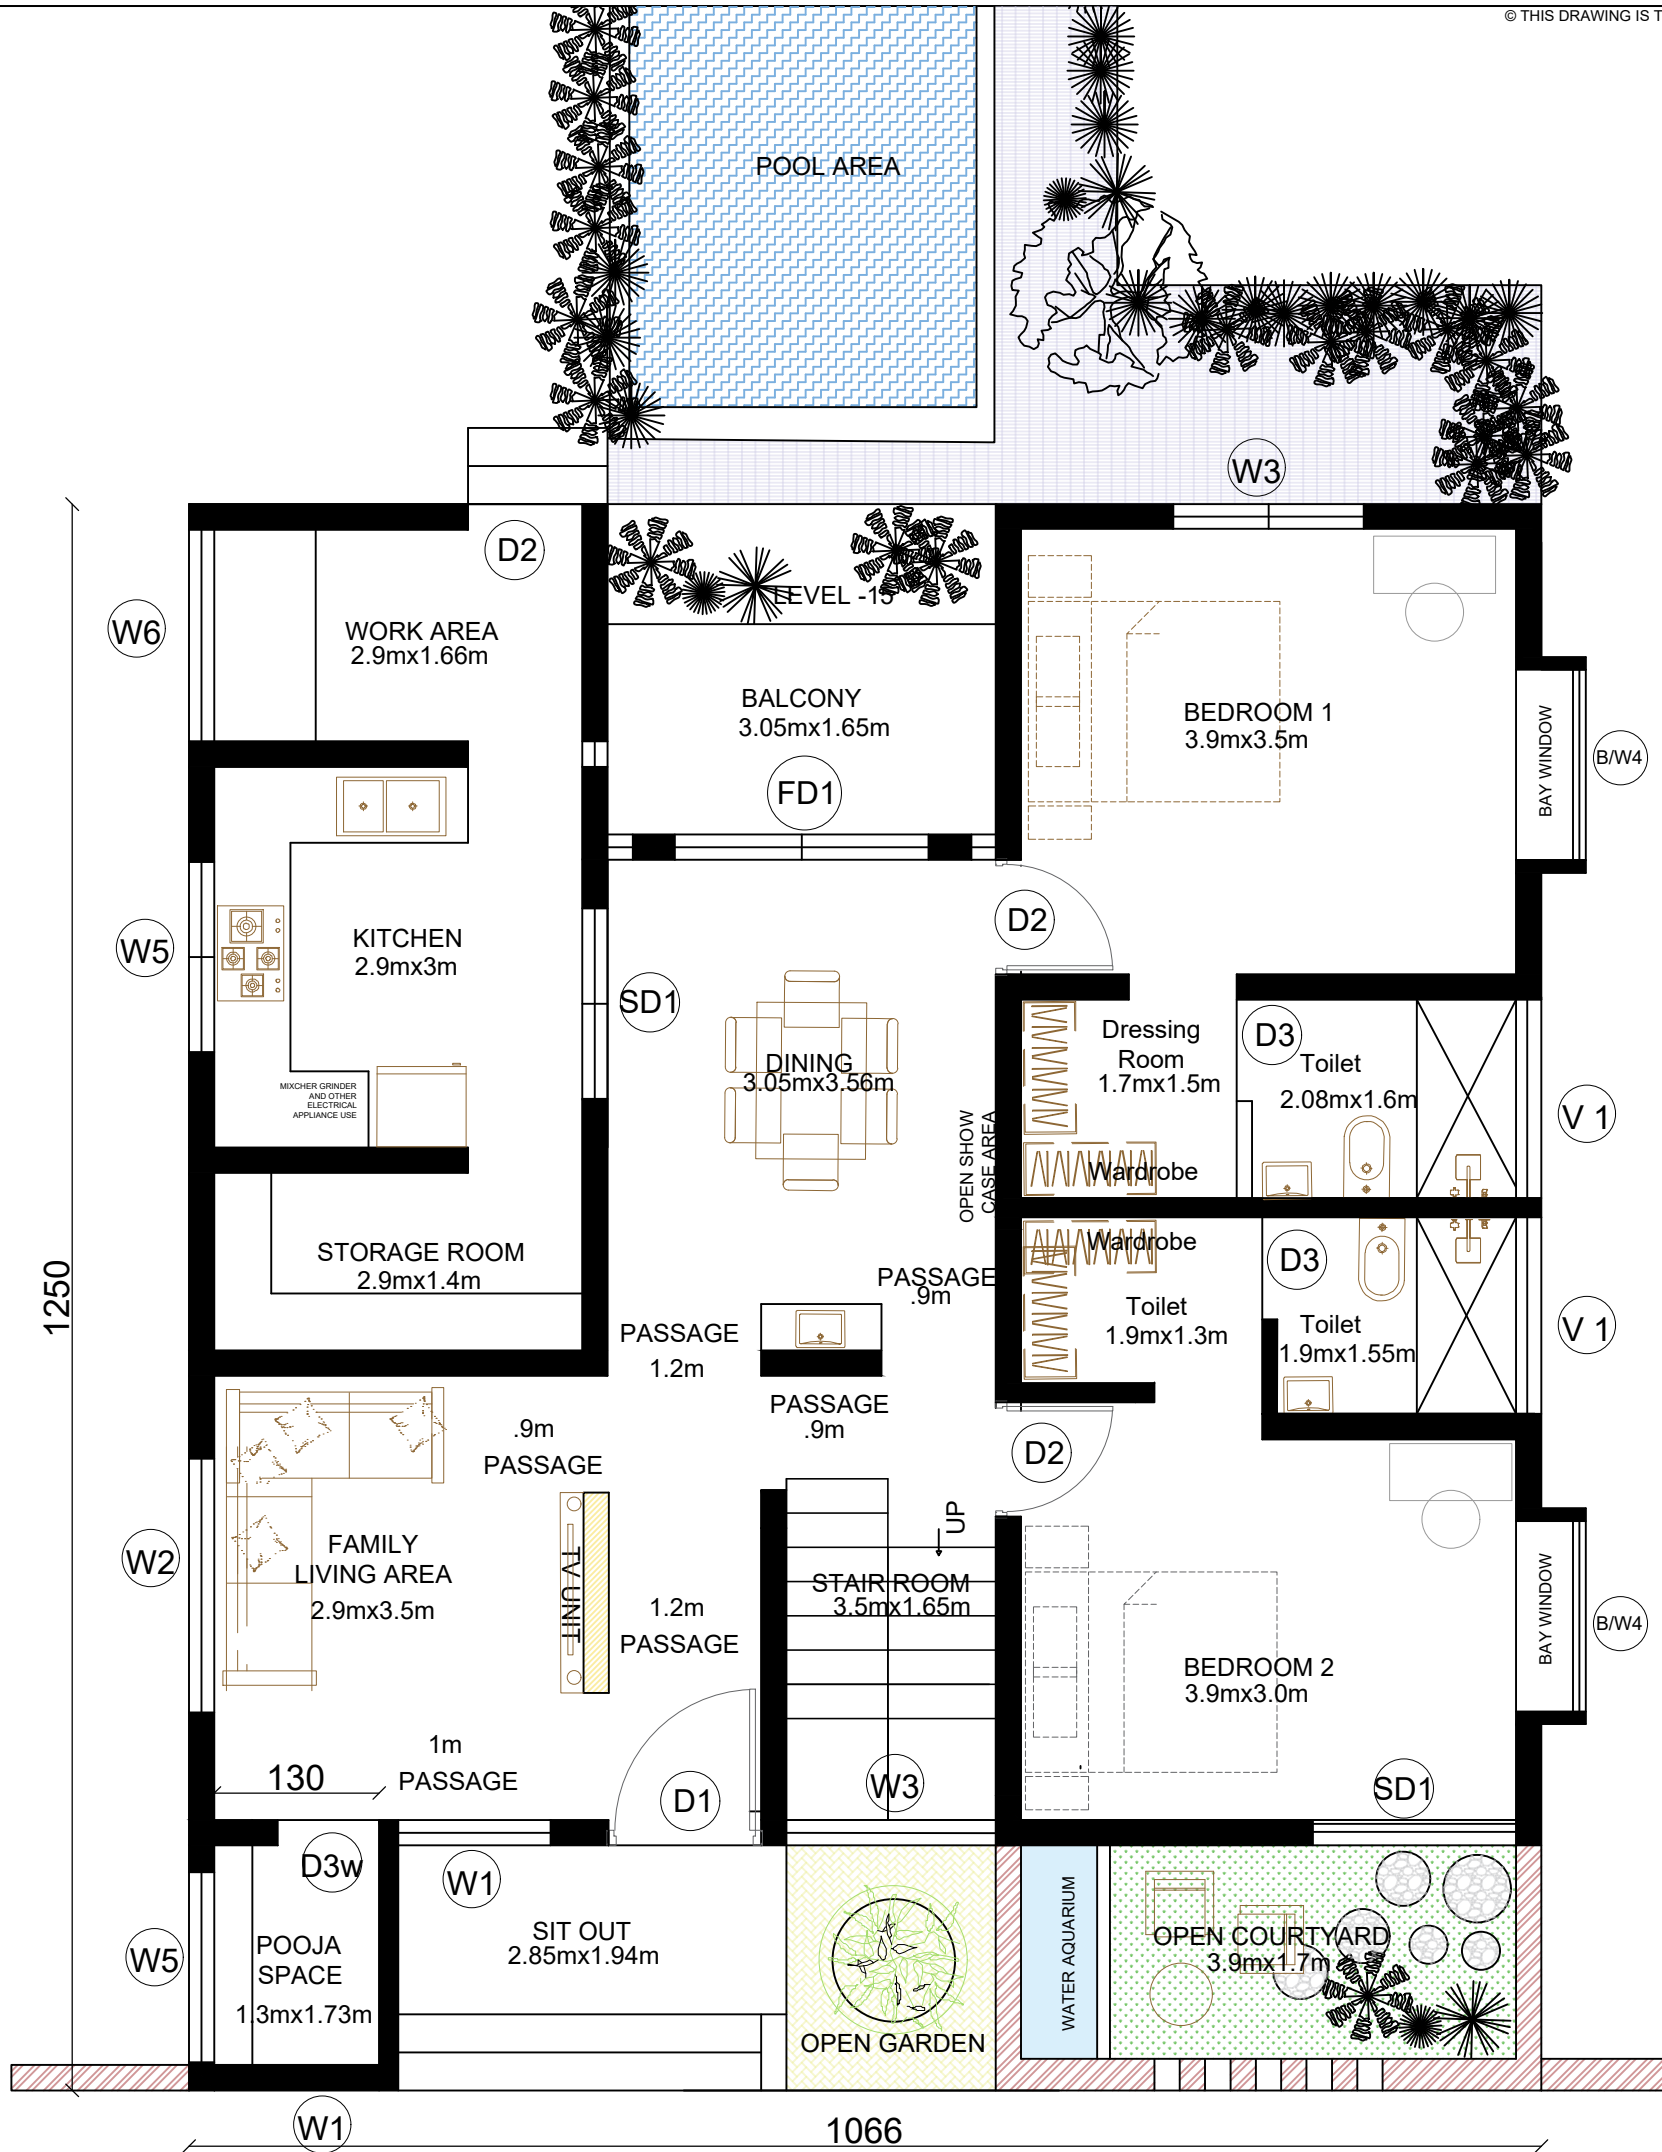

SPECIFICATIONS				
ITEM	WIDTH	HEIGHT	nums	SILL lvl
DOOR D ₁	120	210	1	SILL 0
DOOR D ₂	90	210	3	SILL 0
DOOR D ₃ [WOODEN]	80	210	2	SILL 0
DOOR D _{3.1} [FIBRE]	80	210	1	SILL 0
SD SLIDING DOOR	150	210	1	SILL 0
FD FOLDING DOOR	200	210	1	SILL 0
WINDOW W ₁	120	180	1	SILL +30
WINDOW W ₂	200	180	1	SILL +30
WINDOW W ₃	150	180	1	SILL +30
BAY WINDOW W ₄	150	150	2	SILL +60
WINDOW W ₅	150	60	1	SILL +120
WINDOW W ₆	150	110	1	SILL +30
VENTILATOR V ₁	150	50	2	SILL +175

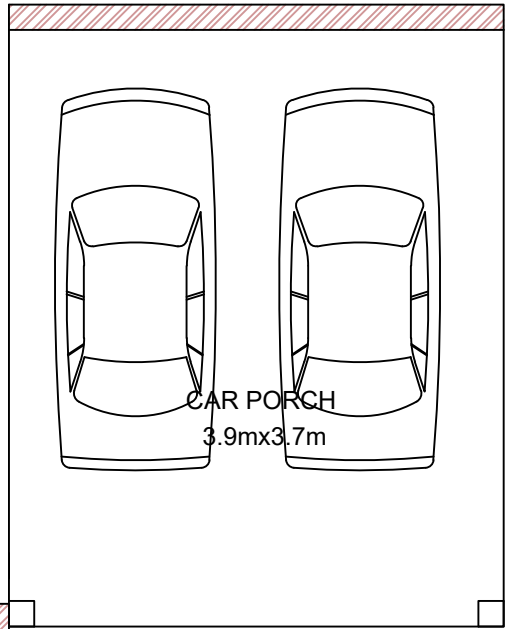

GROUND FLOOR PLAN
AREA -1310 Sqr ft

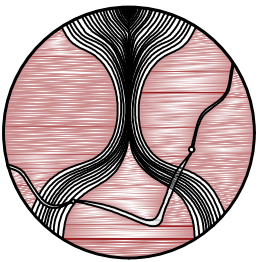

VIDHRITA
STUDIO ARCHITECTS
Architecture | Urban Design&Planning|
Interior Design|Landscape Design|
Art|Product Design

+91 9746235886

SPECIAL NOTES

- Unless mentioned otherwise all dimensions are in centimetres .
- All wall thickness are 15cm .
- All dimensions and levels given in the drawing are finished dimension and levels .
- Drawing shall not be measured, written dimensions to be followed .
- All structural members like beams, columns, lintels etc. shall be provided as per structural drgs and details .
- Leave dowels wherever necessary for architectural elements .
- Unless mentioned otherwise 20 cm sunken in f.f.l of all toilets and 20 cm sunken in f.f.l of all balconies and utilities to be provided -
- Latest revision of drawing should be followed, the drawing previous revision should be canceled.

CLIENT : SREERAKH

LOCATION : KARAKONAM

TYPE : RESIDENCE

TOTAL AREA : 1310 sqft

TITLE : GROUND FLOOR PLAN

SIGN:

ISSUED FOR	☒ Reference	☒ Soft copy
	☐ Construction	☐ Hard copy
	☐ Approval	

DRG NO: DRAWN by: Ar Vighnesh sv

SCALE : N T S CHECKED by: Ar Vighnesh sv

DATE : 01/09/2025 REVISION NO:

